PORTFOLIO

Luisa Kortner



ALPINE FLUX
SENSING ARCHITECTURES FOR THE ALPS


ALPINe SHeLL


Conceived within the framework of Alpine Flux, the project proposes a year-round space for learning, observation, and retreat embedded in the alpine landscape at 1,100 meters altitude. Positioned along a hiking route, the building becomes a point to reach within the territory, a pause in the journey for hikers, skiers, and visitors. Neither purely a library nor solely an observation platform, it operates as an in-between space for reading, resting, working, gathering, and attentive observation.

The circular interior accommodates a library and flexible learning space oriented toward panoramic views, offering a warm and protected refuge during winter and a luminous, naturally shaded environment in summer.





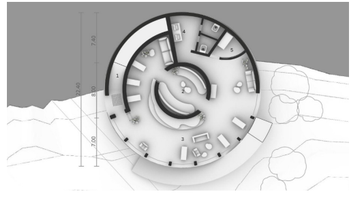

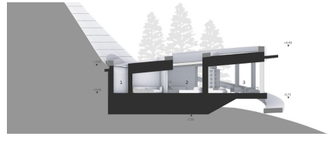



The roof forms the conceptual core of the project : in winter it becomes a snow covered slope shaped by climate and use; while in summer, it functions as a walkable garden and viewing platform extending the hiking path.


Conceived as a long-term architectural instrument, the building evolves with the landscape, archiving environmental change and remaining a resilient interface between humans and the mountain.


HÔTEL SUSPENDUE

INSPIRED BY THE MAISON SUSPENDUE





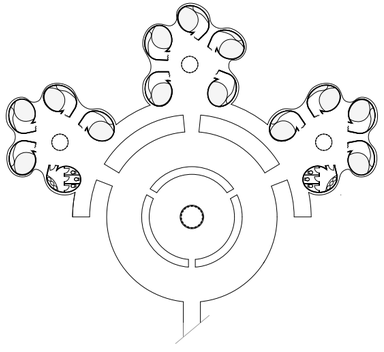


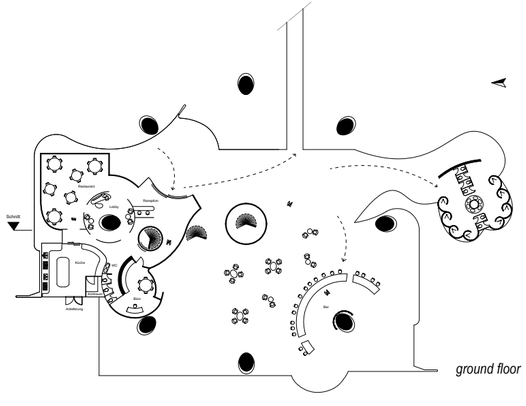


ground floor


The hotel translates Paul Nelson's Maison Suspendue (1938) into a sustainable design for the 21st century. An organic exoskeleton made of natural fibers supports floating sleeping capsules crafted from bamboo. Through fluid spatial transitions and sculptural ramps, architecture and nature merge.

Self-sufficient systems, such as rainwater harvesting and organic photovoltaics, combine radical lightweight construction with ecological responsibility.

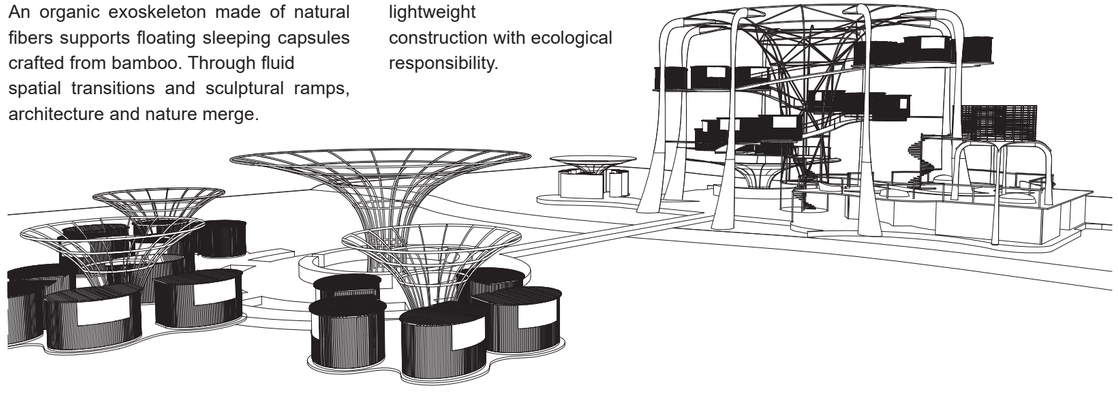

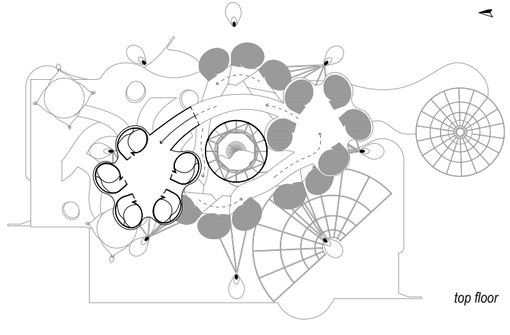


top floor

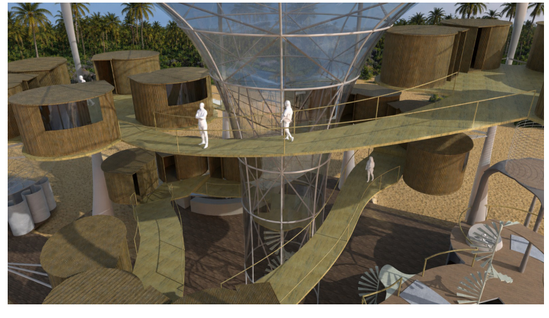

ALBERO

Dove le radici uniscono

Wo Wurzeln verbinden

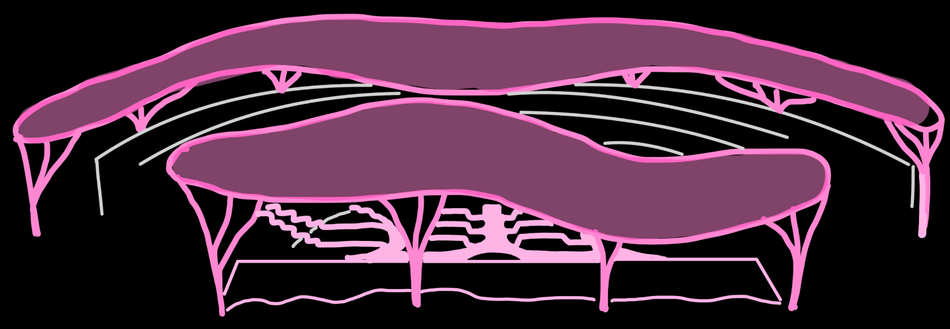

Der Baum als neues Leben des Theaters

Mein Entwurf basiert auf der Idee, das historische Theater als einen Baum neu zu interpretieren.

Der Baum steht dabei für Leben, Wachstum und Veränderung. So wie ein Baum mit seiner Umgebung verwurzelt ist, bleibt auch mein Entwurf mit der Geschichte des Ortes verbunden.

Das Herzstück bilden die Wurzeln, sie stehen für den Ursprung und die Lebensgrundlage des Baumes. In meinem Theater werden sie zu organischen Sitzmöglichkeiten, die sich durch den Zuschauerraum ziehen und schließlich in die Bühne übergehen.


Dadurch entsteht eine Verbindung zwischen Publikum und Bühne. Denn genauso wie ein Baum ohne seine Wurzeln nicht leben kann, kann ein Theater ohne seine Zuschauer nicht bestehen. Die Menschen werden zum Mittelpunkt und zur Lebensgrundlage des Ortes.

Die Wurzeln breiten sich außerdem in die beschädigten historischen Sitzreihen aus und schaffen dort neue Aufenthaltsmöglichkeiten. So entsteht aus dem Alten etwas Neues, ohne die Geschichte des Theaters zu verdrängen.

Über dem Zuschauerraum bildet eine baumartige Stahlkonstruktion die Krone. Sie übernimmt wie ein Baum eine schützende Funktion und wird in Teilbereichen durch Kletterpflanzen begrünt.


Mein Ziel ist es, das Theater nicht einfach nur wiederherzustellen, sondern ihm neues Leben zu geben. Der Baum wird dabei zum Sinnbild eines Ortes, der weiterwächst, sich verändert und Menschen wieder zusammenbringt.

PIKTOGRAMM

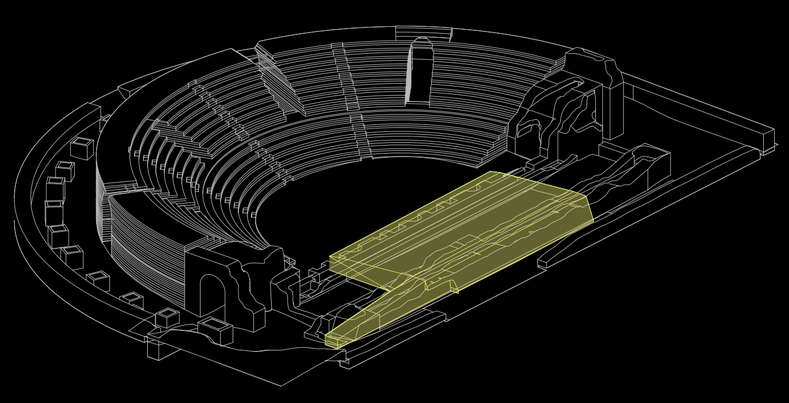


Freistellen

Die alte Bühne wird entfernt und macht Platz für Neues.

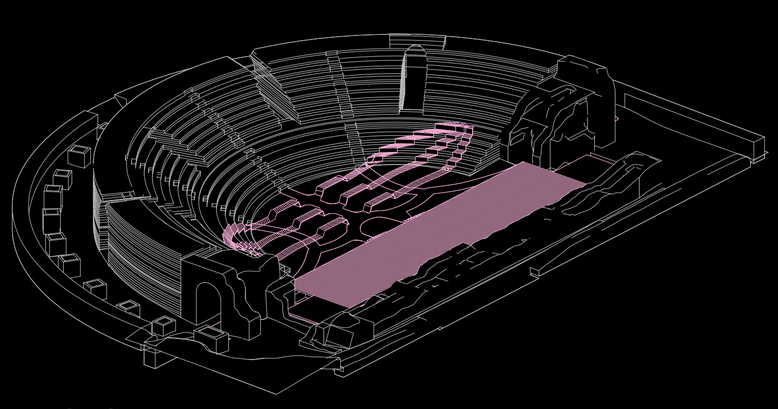

Verbinden


Die Wurzelbänke verbinden die Sitzbereiche und die neue Bühne.

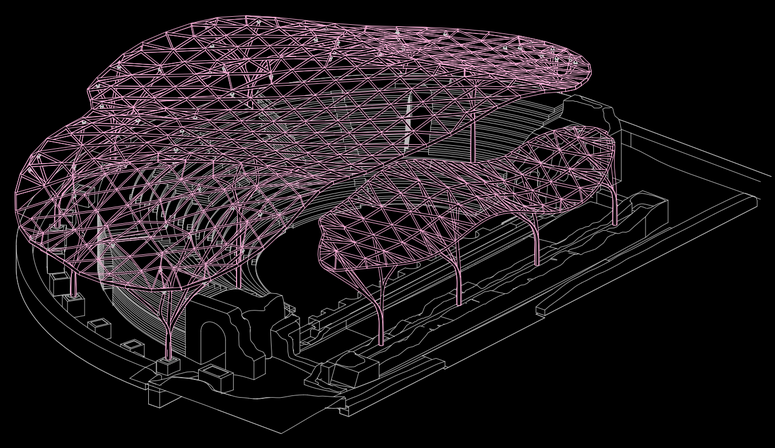

Überdachen


Das Dach verbindet Bühne und Publikum zu einem gemeinsamen Raum.

SCHNITT

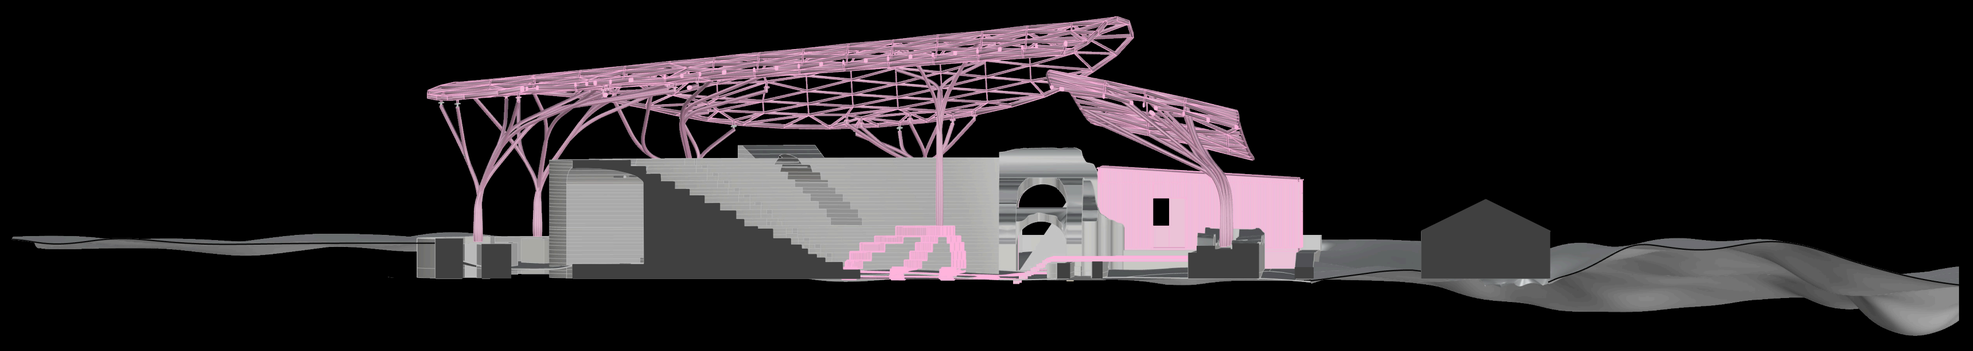


1:200

GRUNDRISS

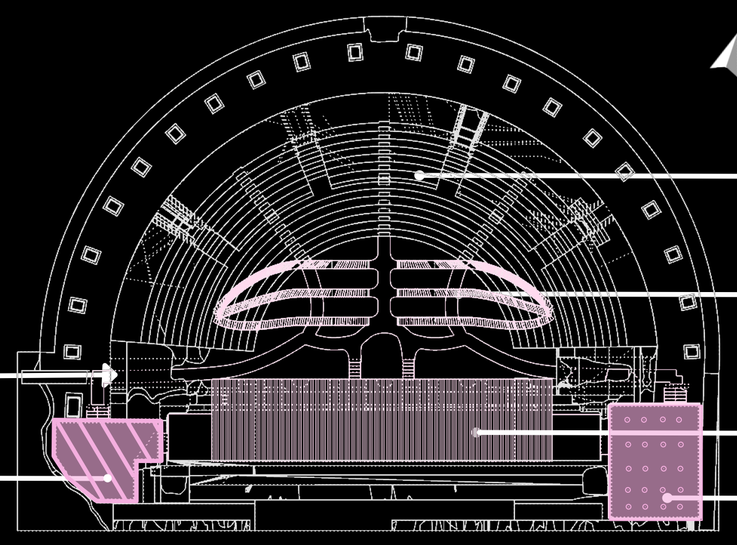


1:333

RÄUMLICHE SCHNITTANSICHT

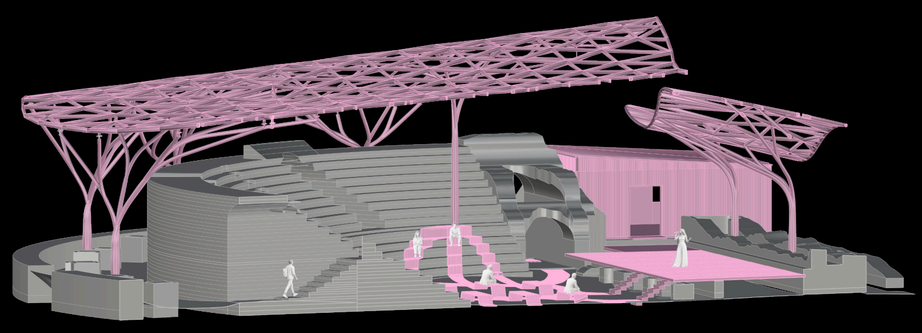

1:200

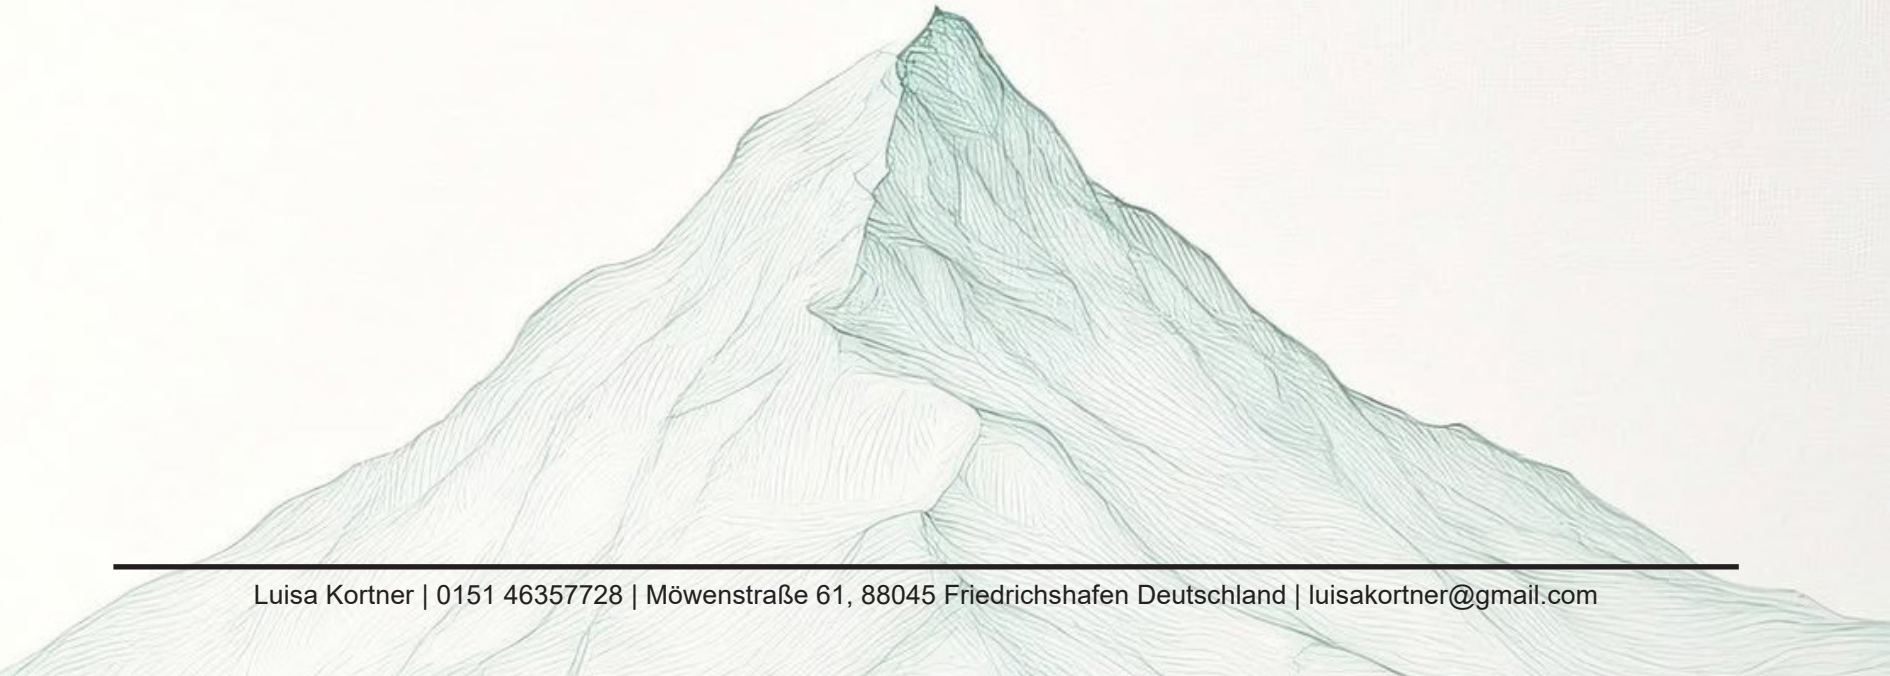

Luisa Kortner | 0151 46357728 | Möwenstraße 61, 88045 Friedrichshafen Deutschland | luisakortner@gmail.com